




GENERAL NOTES :
DO NOT SCALE THIS DRAWING, ONLY STATED DIMENSIONS ARE TO BE CONSIDERED.
IT IS NOT ALLOWED TO COPY OR REPRODUCE IT'S CONTENTS IN ANY FORM EXCEPT FOR THE PURPOSE WHICH IT IS INTENDED WITHOUT THE ABOVE CONSULTANT'S AUTHORITY.
CONTRACTOR TO VERIFY THE DETAIL / INFORMATION GIVEN IN THIS DRAWING, ANY DISCREPANCIES SHALL BE BROUGHT TO ENGINEERS ATTENTION PRIOR TO COMMENCEMENT OF WORK, FAILURE TO COMPLY WITH THE ABOVE WILL BE CONTRACTORS LIABILITY.

CONSULTANT

INTERIOR DESIGNER

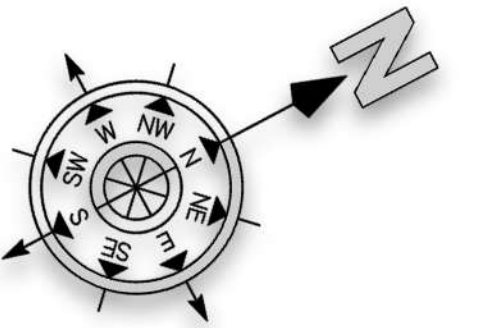

Rev.	Date	Description.	By	

PURPOSE OF ISSUE
ISSUED FOR TENDER

PROJECT TITLE

G+04 RESIDENTIAL BUILDING

CLIENT


ALASAD REAL ESTATE DEVELOPMENT LLC

PROJECT NO.
25-011 - Takmeel - Dubai South Building


DRAWING TITLE

GYM & LOCKERS

DATE	SHT. SIZE	SCALE	DRAWN	CHECKED	APPROVED
JUNE 2025	A1		CJA	YSR	YSR
PAGE NO	DRAWING ID		NORTH		REVISION

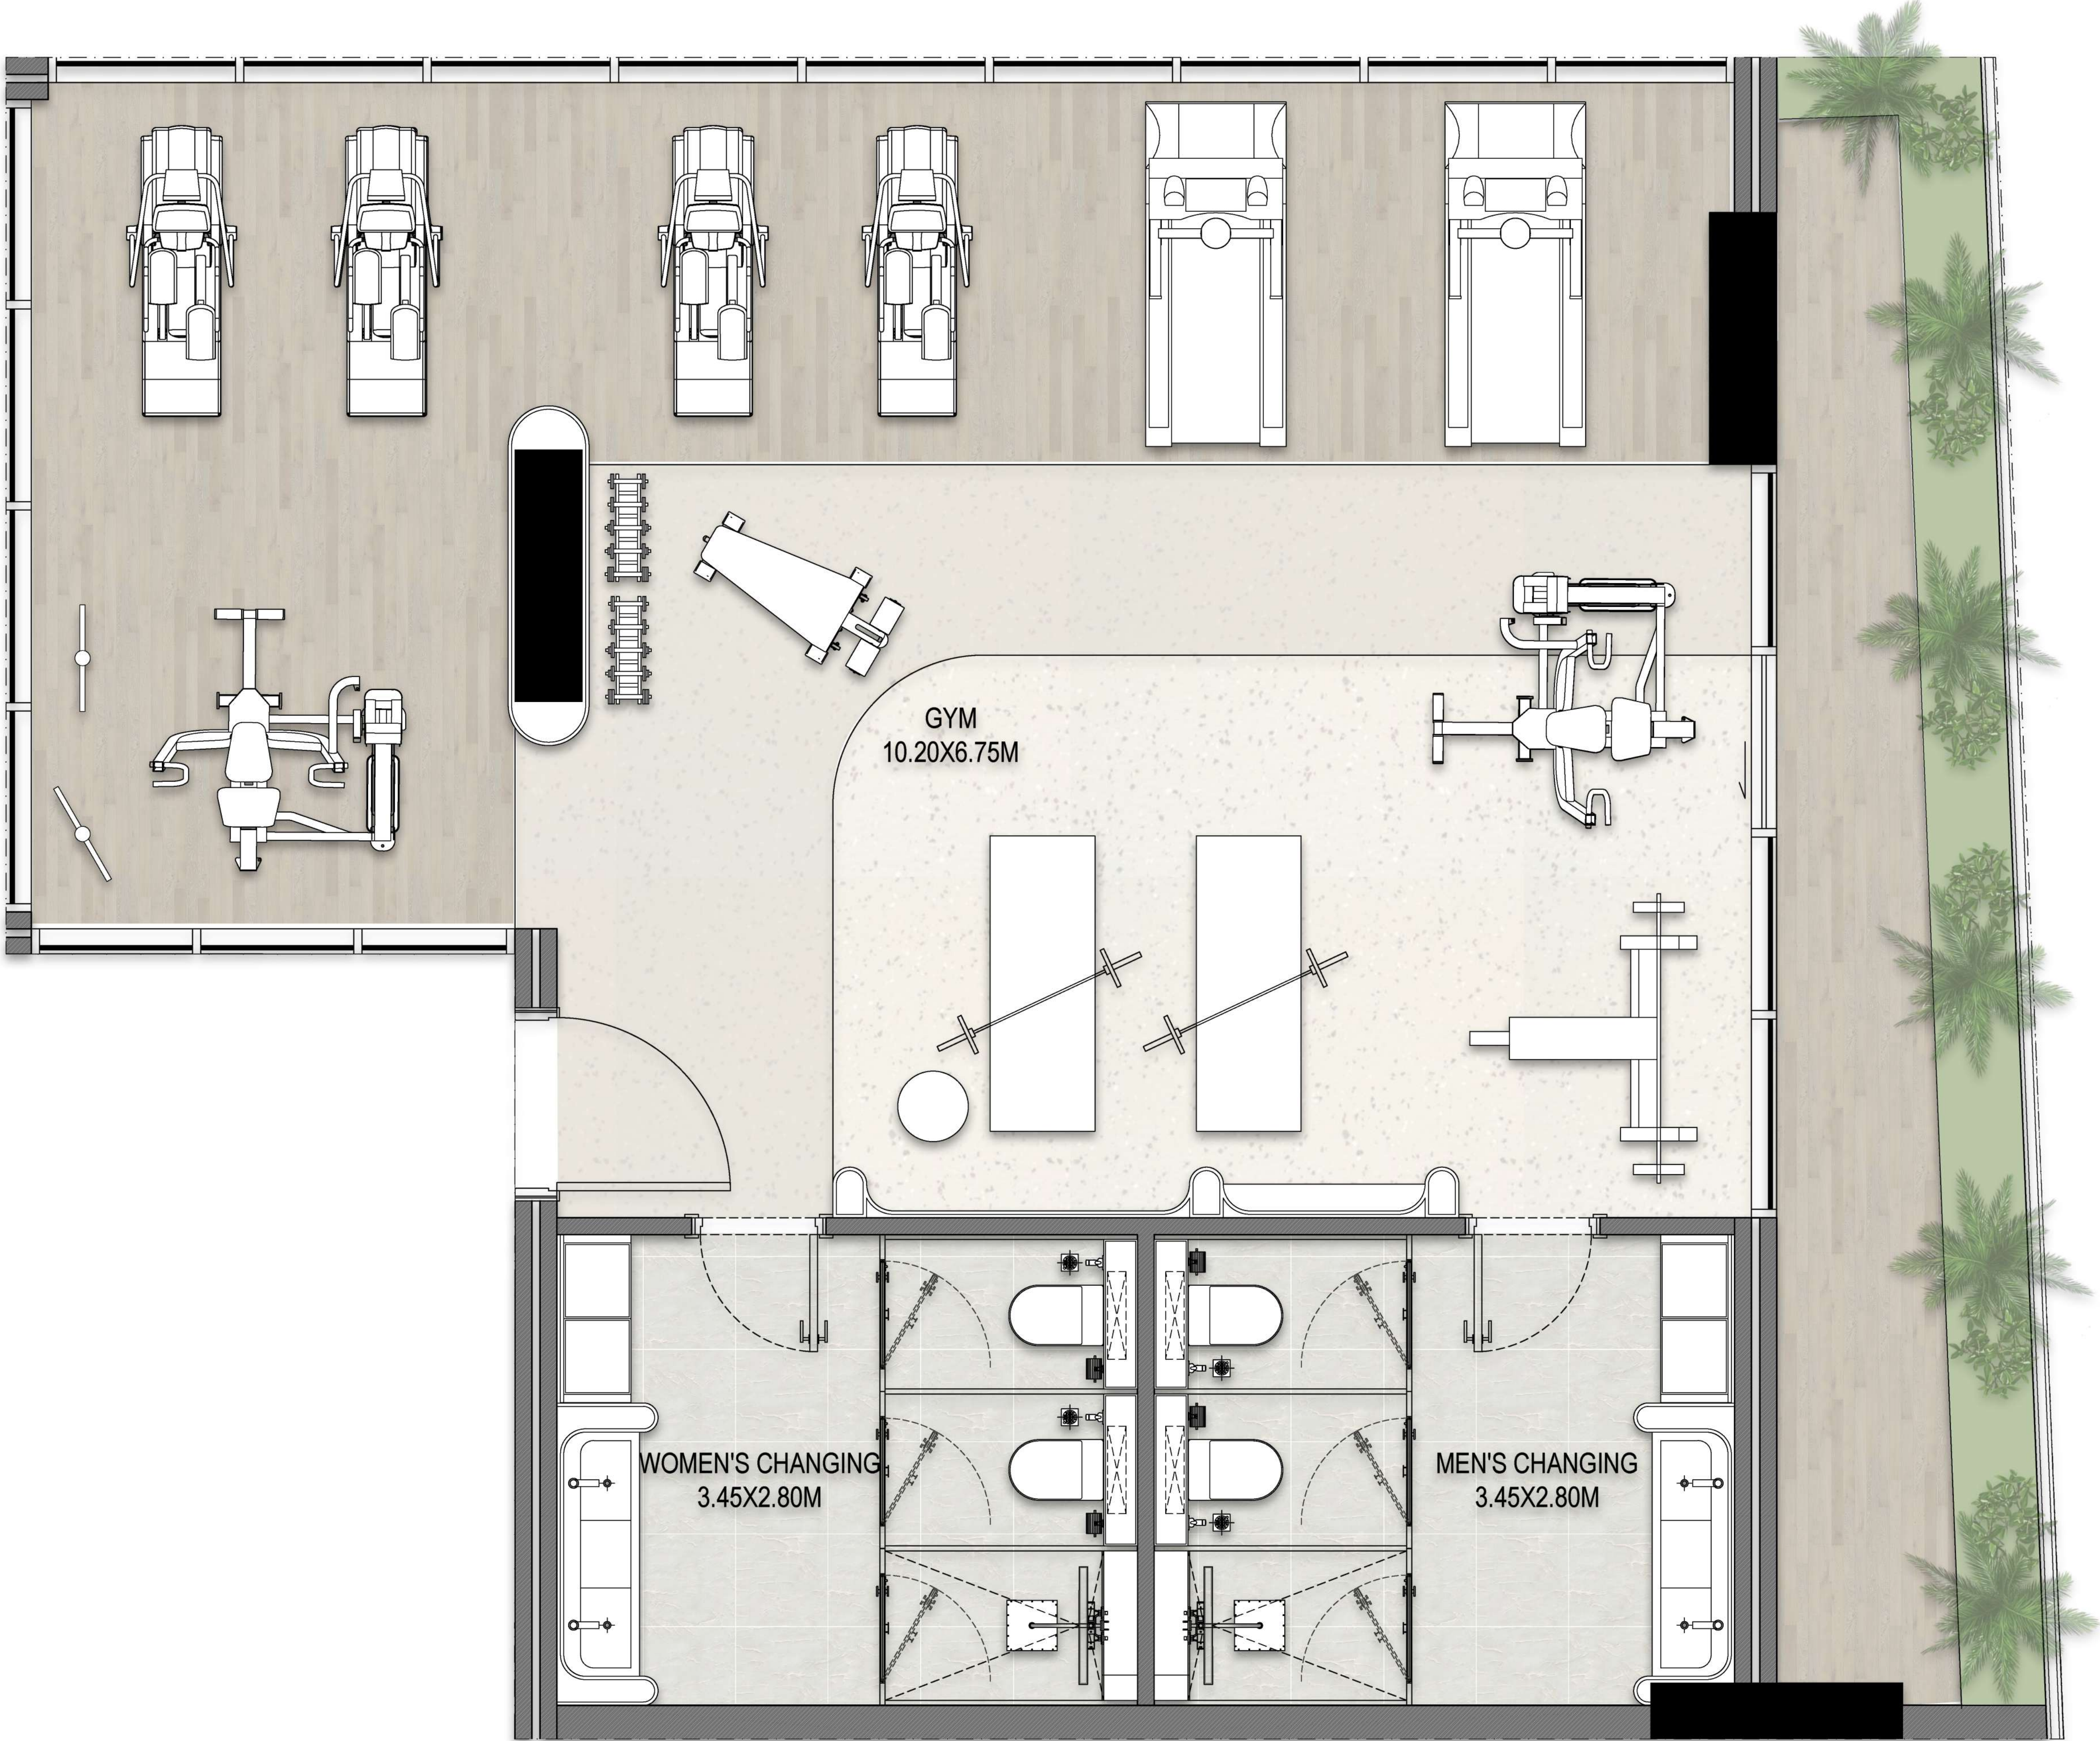

01 GYM & LOCKERS
SCALE 1:100@A1

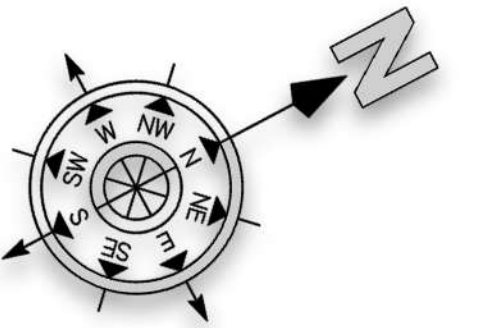

GENERAL NOTES :
DO NOT SCALE THIS DRAWING, ONLY STATED DIMENSIONS ARE TO BE CONSIDERED.
IT IS NOT ALLOWED TO COPY OR REPRODUCE IT'S CONTENTS IN ANY FORM EXCEPT FOR THE PURPOSE WHICH IT IS INTENDED WITHOUT THE ABOVE CONSULTANT'S AUTHORITY.
CONTRACTOR TO VERIFY THE DETAIL / INFORMATION GIVEN IN THIS DRAWING, ANY DISCREPANCIES SHALL BE BROUGHT TO ENGINEERS ATTENTION PRIOR TO COMMENCEMENT OF WORK, FAILURE TO COMPLY WITH THE ABOVE WILL BE CONTRACTORS LIABILITY.

CONSULTANT

INTERIOR DESIGNER



Rev.	Date	Description.	By
------	------	--------------	----

PURPOSE OF ISSUE
ISSUED FOR TENDER

PROJECT TITLE

G+04 RESIDENTIAL BUILDING


CLIENT

ALASAD REAL ESTATE
DEVELOPMENT LLC


PROJECT NO.
25-011 - Takmeel - Dubai South Building

DRAWING TITLE
STUDIO


DATE	SHT. SIZE	SCALE	DRAWN	CHECKED	APPROVED
JUNE 2025	A1		CJA	YSR	YSR
PAGE NO	DRAWING ID	NORTH	REVISION		

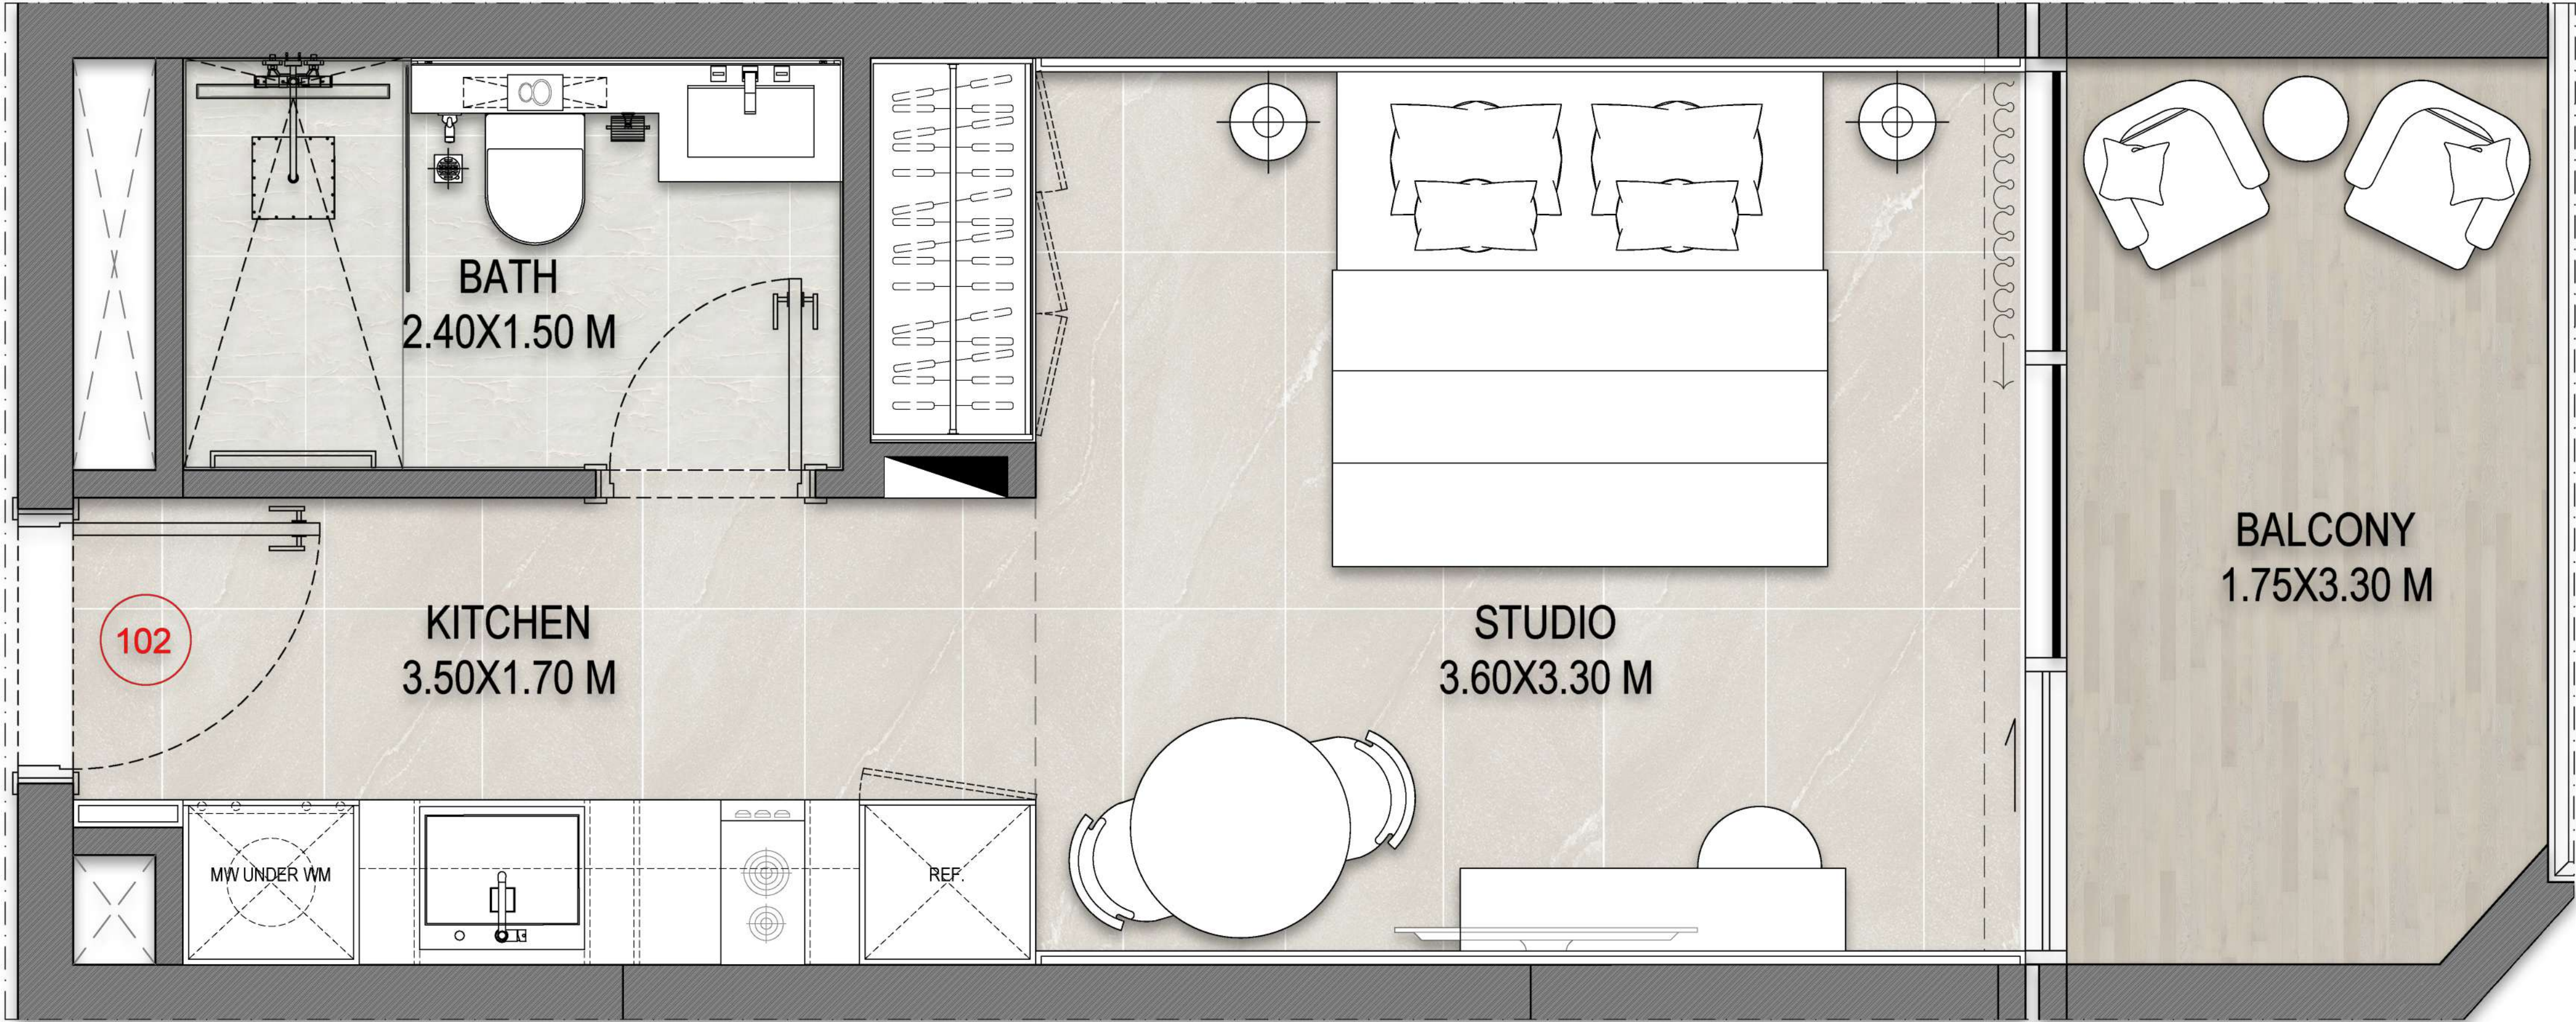

01 STUDIO
SCALE 1:100@A1

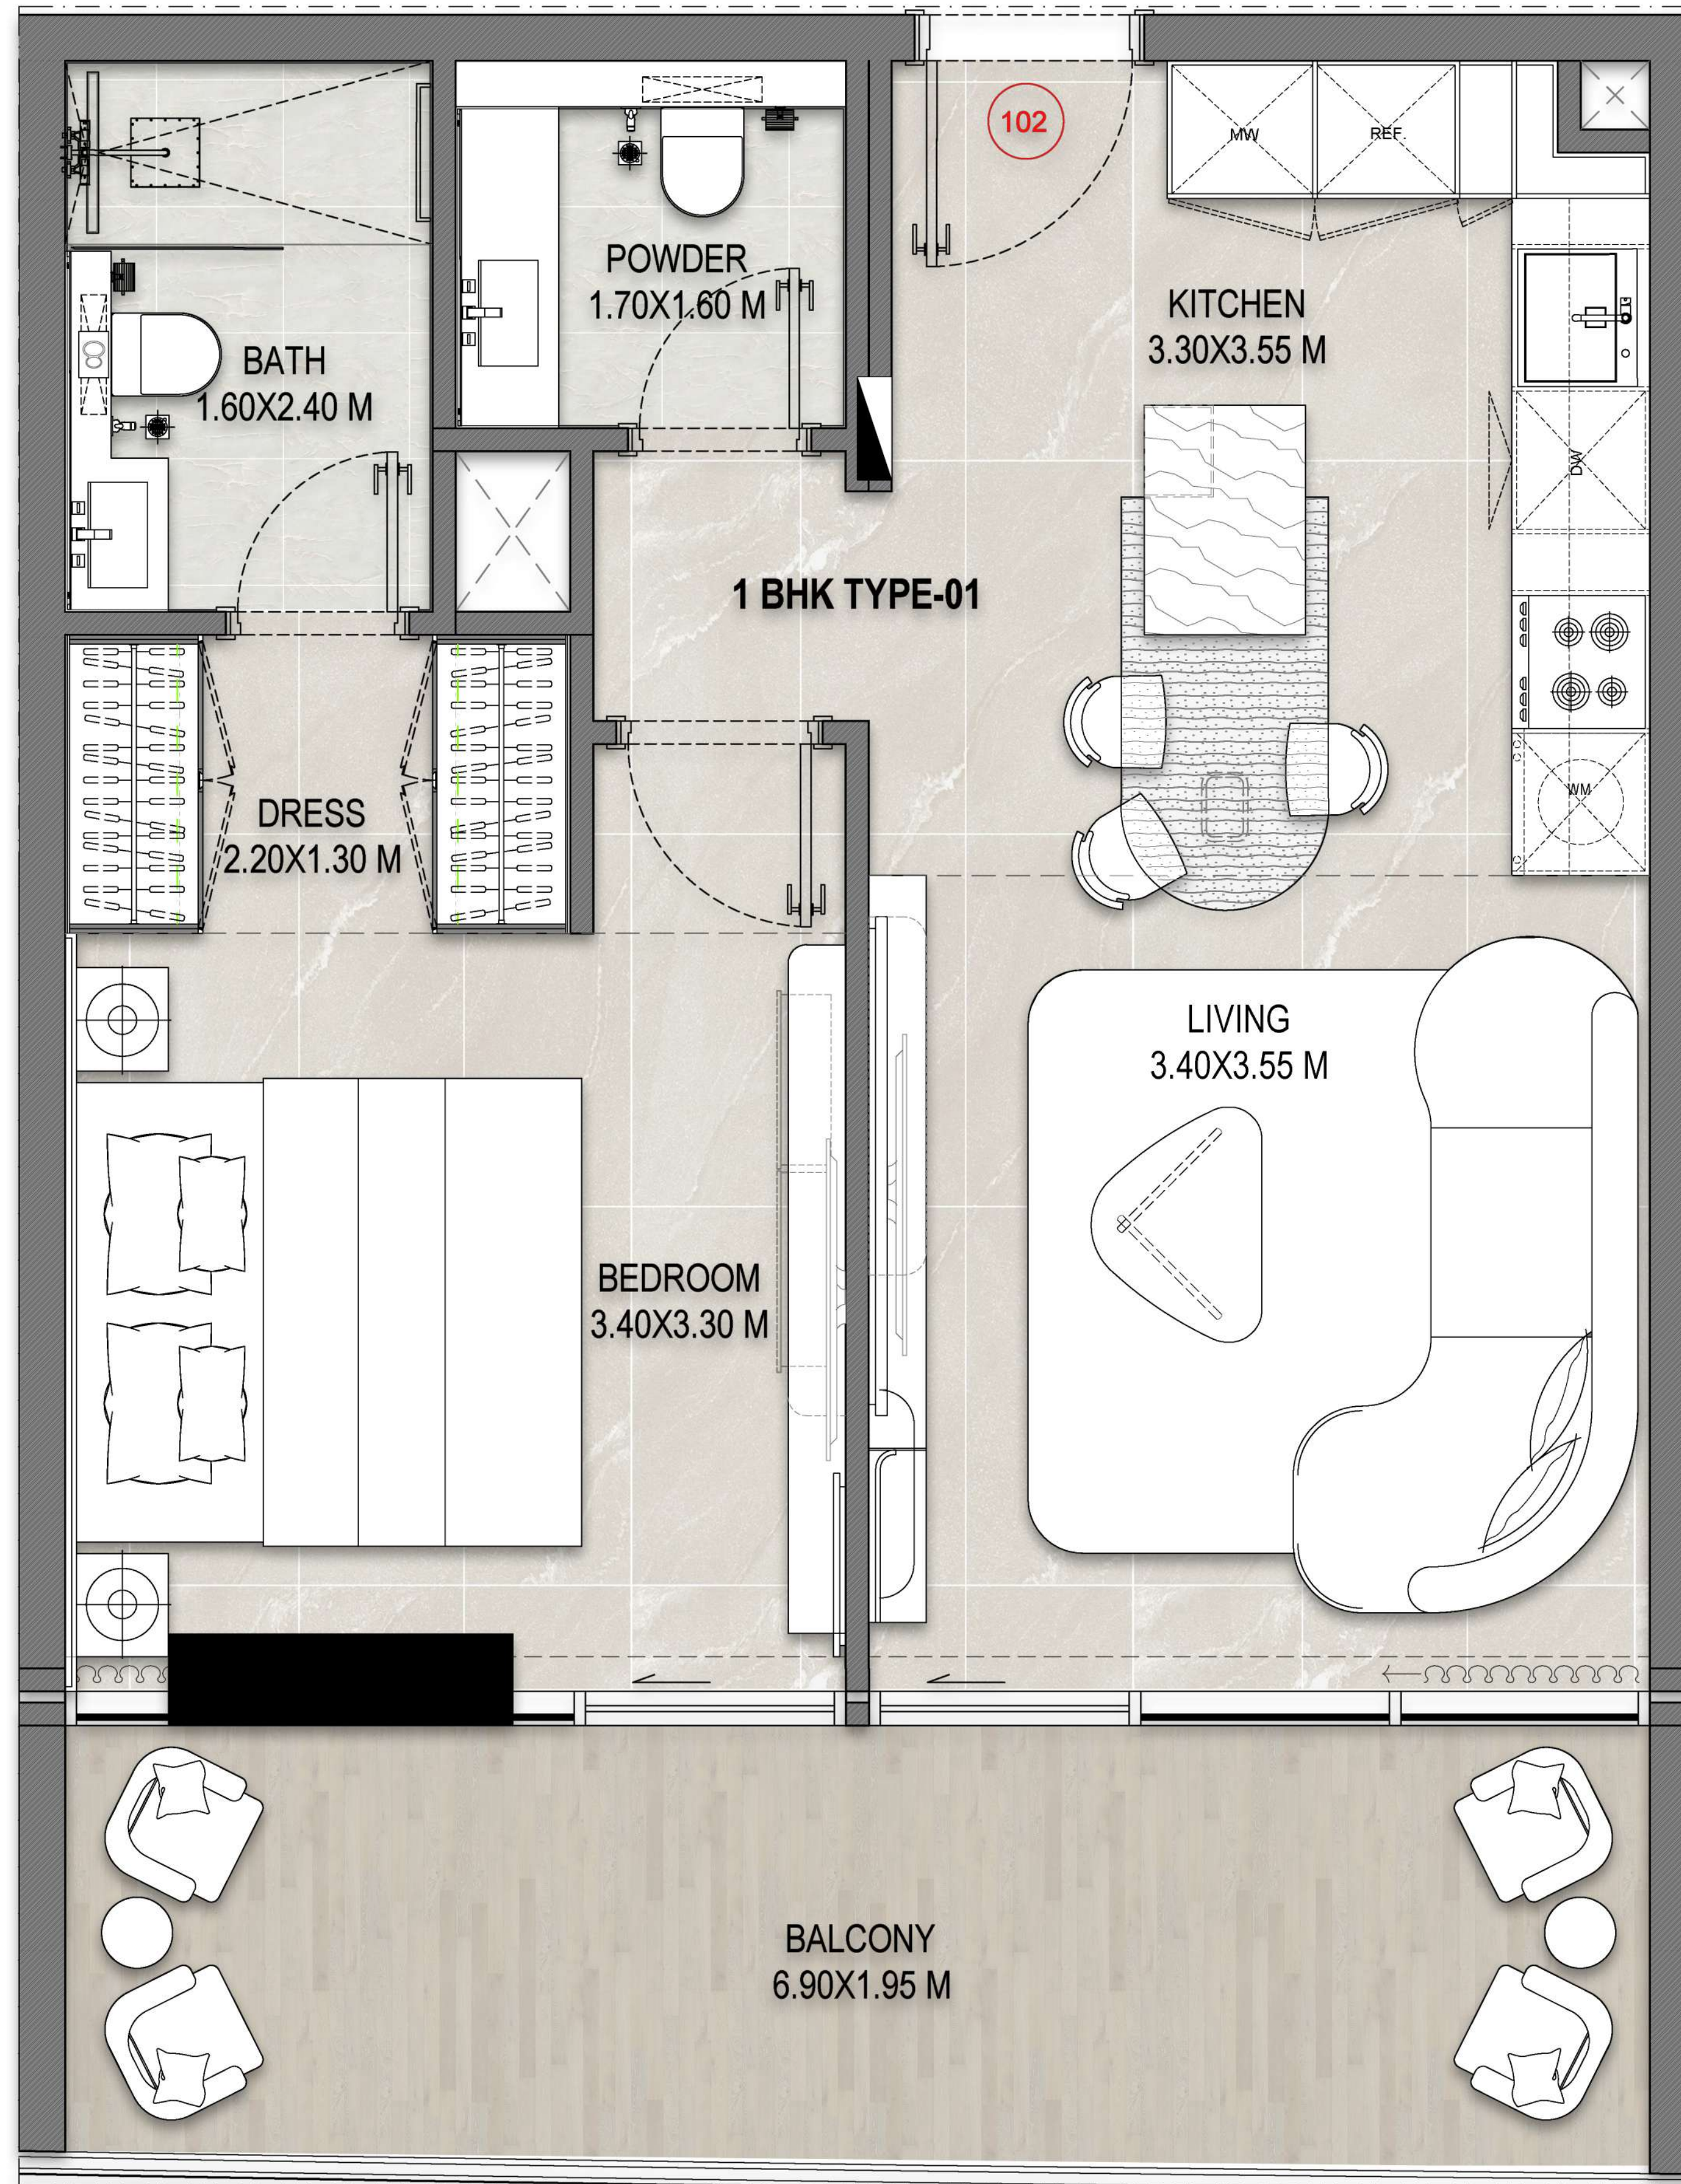

01 1 BHK TYPE-01
SCALE 1:100@A1

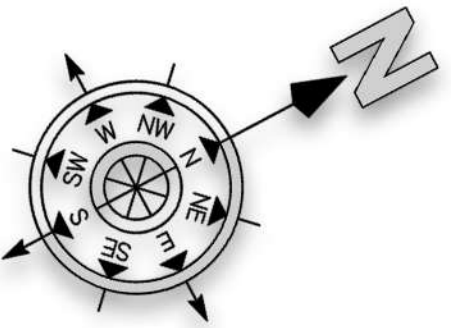

GENERAL NOTES :
DO NOT SCALE THIS DRAWING, ONLY STATED DIMENSIONS ARE TO BE CONSIDERED.
IT IS NOT ALLOWED TO COPY OR REPRODUCE IT'S CONTENTS IN ANY FORM EXCEPT FOR THE PURPOSE WHICH IT IS INTENDED WITHOUT THE ABOVE CONSULTANT'S AUTHORITY.
CONTRACTOR TO VERIFY THE DETAIL / INFORMATION GIVEN IN THIS DRAWING, ANY DISCREPANCIES SHALL BE BROUGHT TO ENGINEERS ATTENTION PRIOR TO COMMENCEMENT OF WORK, FAILURE TO COMPLY WITH THE ABOVE WILL BE CONTRACTORS LIABILITY.

CONSULTANT

INTERIOR DESIGNER



Rev.	Date	Description.	By

PURPOSE OF ISSUE
ISSUED FOR TENDER

PROJECT TITLE

G+04 RESIDENTIAL BUILDING

CLIENT


ALASAD REAL ESTATE DEVELOPMENT LLC

PROJECT NO.
25-011 - Takmeel - Dubai South Building

DRAWING TITLE


1 BHK TYPE-01

DATE	SHT. SIZE	SCALE	DRAWN	CHECKED	APPROVED
JUNE 2025	A1		CJA	YSR	YSR
PAGE NO	DRAWING ID		NORTH	REVISION	

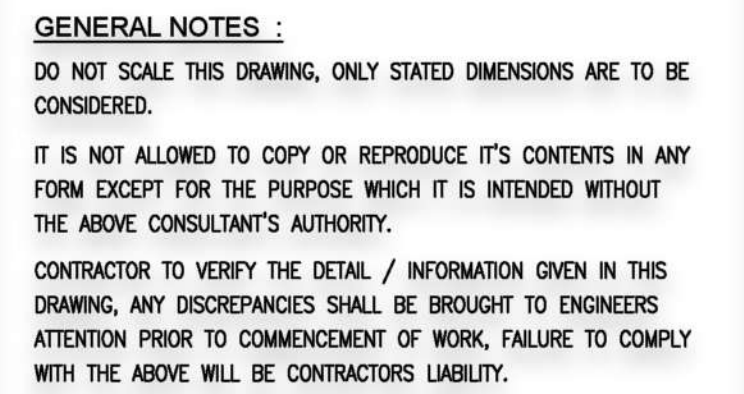


DATE	SHT. SIZE	SCALE	DRAWN	CHECKED	APPROVED
JUNE 2025	A1		CJA	YSR	YSR
PAGE NO	DRAWING ID			NORTH	REVISION

1:100@A1

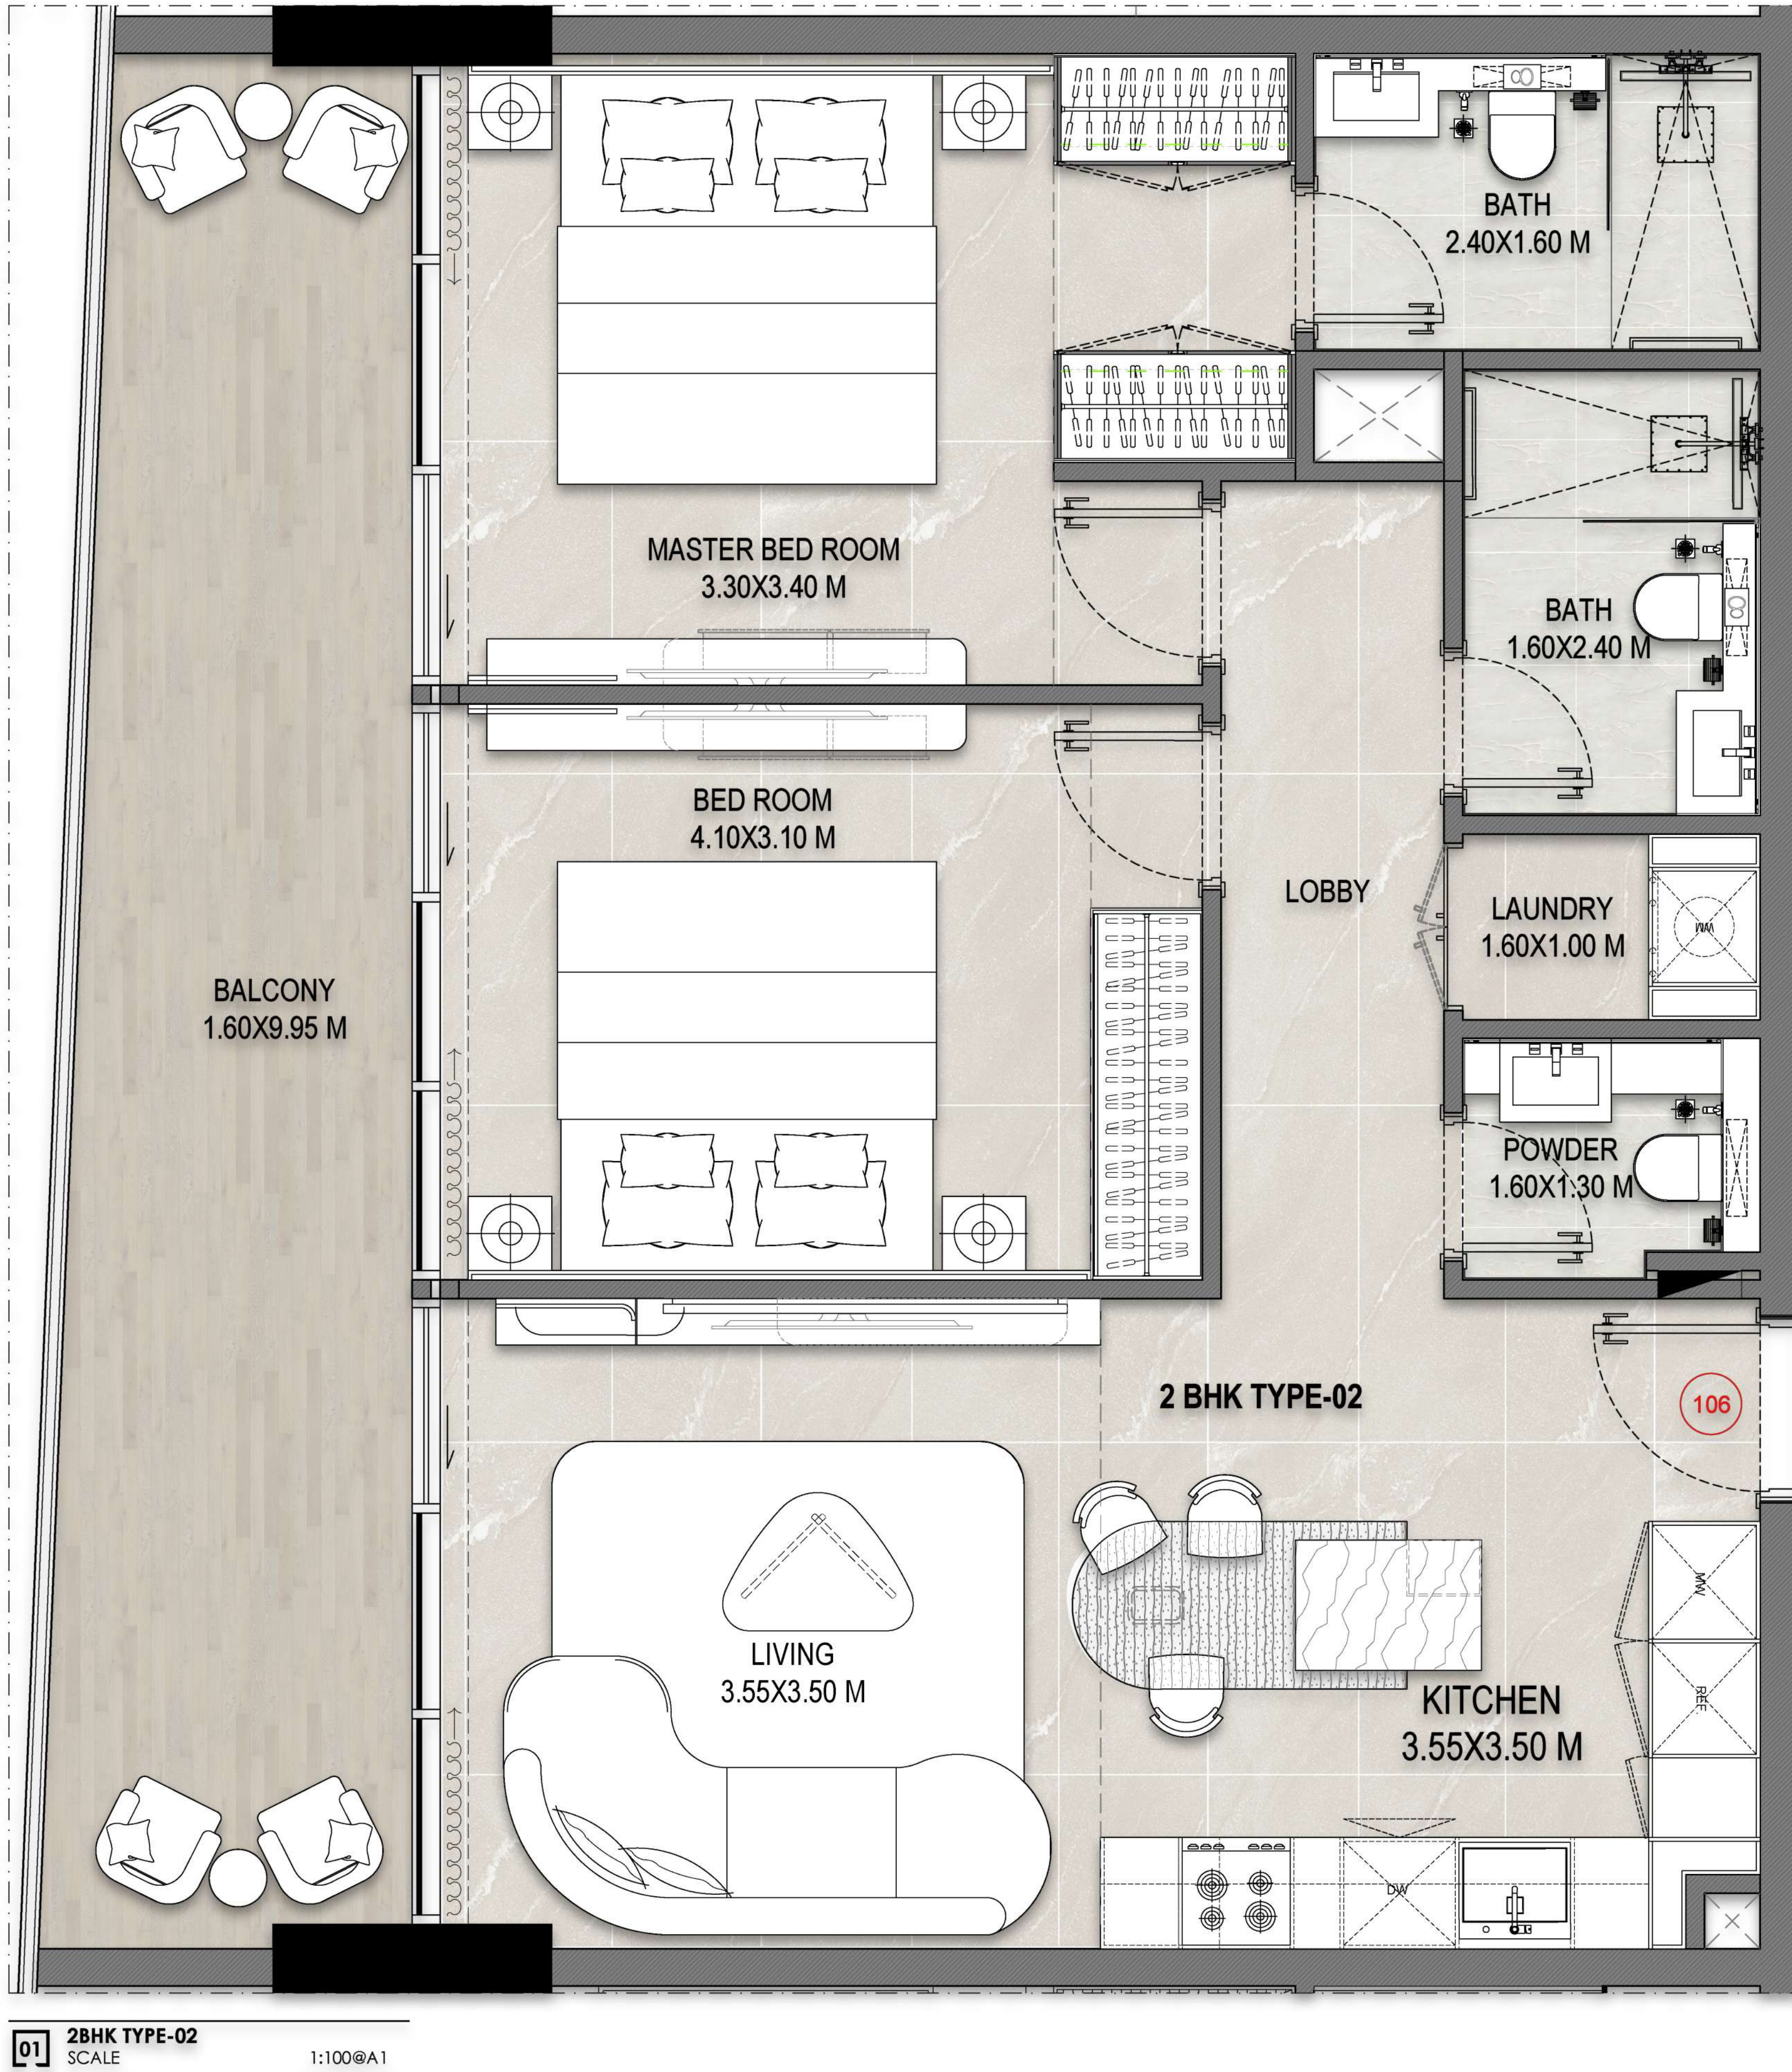

01 2BHK TYPE-02
SCALE 1:100@A1

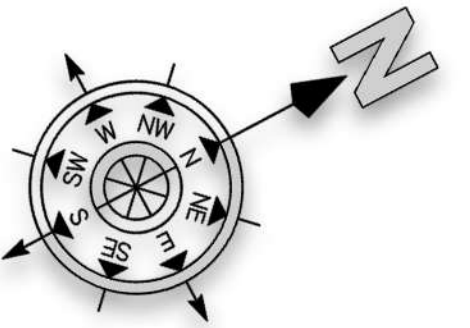

GENERAL NOTES :
DO NOT SCALE THIS DRAWING, ONLY STATED DIMENSIONS ARE TO BE CONSIDERED.
IT IS NOT ALLOWED TO COPY OR REPRODUCE IT'S CONTENTS IN ANY FORM EXCEPT FOR THE PURPOSE WHICH IT IS INTENDED WITHOUT THE ABOVE CONSULTANT'S AUTHORITY.
CONTRACTOR TO VERIFY THE DETAIL / INFORMATION GIVEN IN THIS DRAWING, ANY DISCREPANCIES SHALL BE BROUGHT TO ENGINEERS ATTENTION PRIOR TO COMMENCEMENT OF WORK, FAILURE TO COMPLY WITH THE ABOVE WILL BE CONTRACTORS LIABILITY.

CONSULTANT

INTERIOR DESIGNER



Rev.	Date	Description.	By

PURPOSE OF ISSUE
ISSUED FOR TENDER


PROJECT TITLE
G+04 RESIDENTIAL BUILDING

CLIENT
ALASAD REAL ESTATE DEVELOPMENT LLC


PROJECT NO.
25-011 - Takmeel - Dubai South Building

DRAWING TITLE
2BHK TYPE-02

DATE	SHT. SIZE	SCALE	DRAWN	CHECKED	APPROVED
JUNE 2025	A1		CJA	YSR	YSR
PAGE NO	DRAWING ID	NORTH		REVISION	

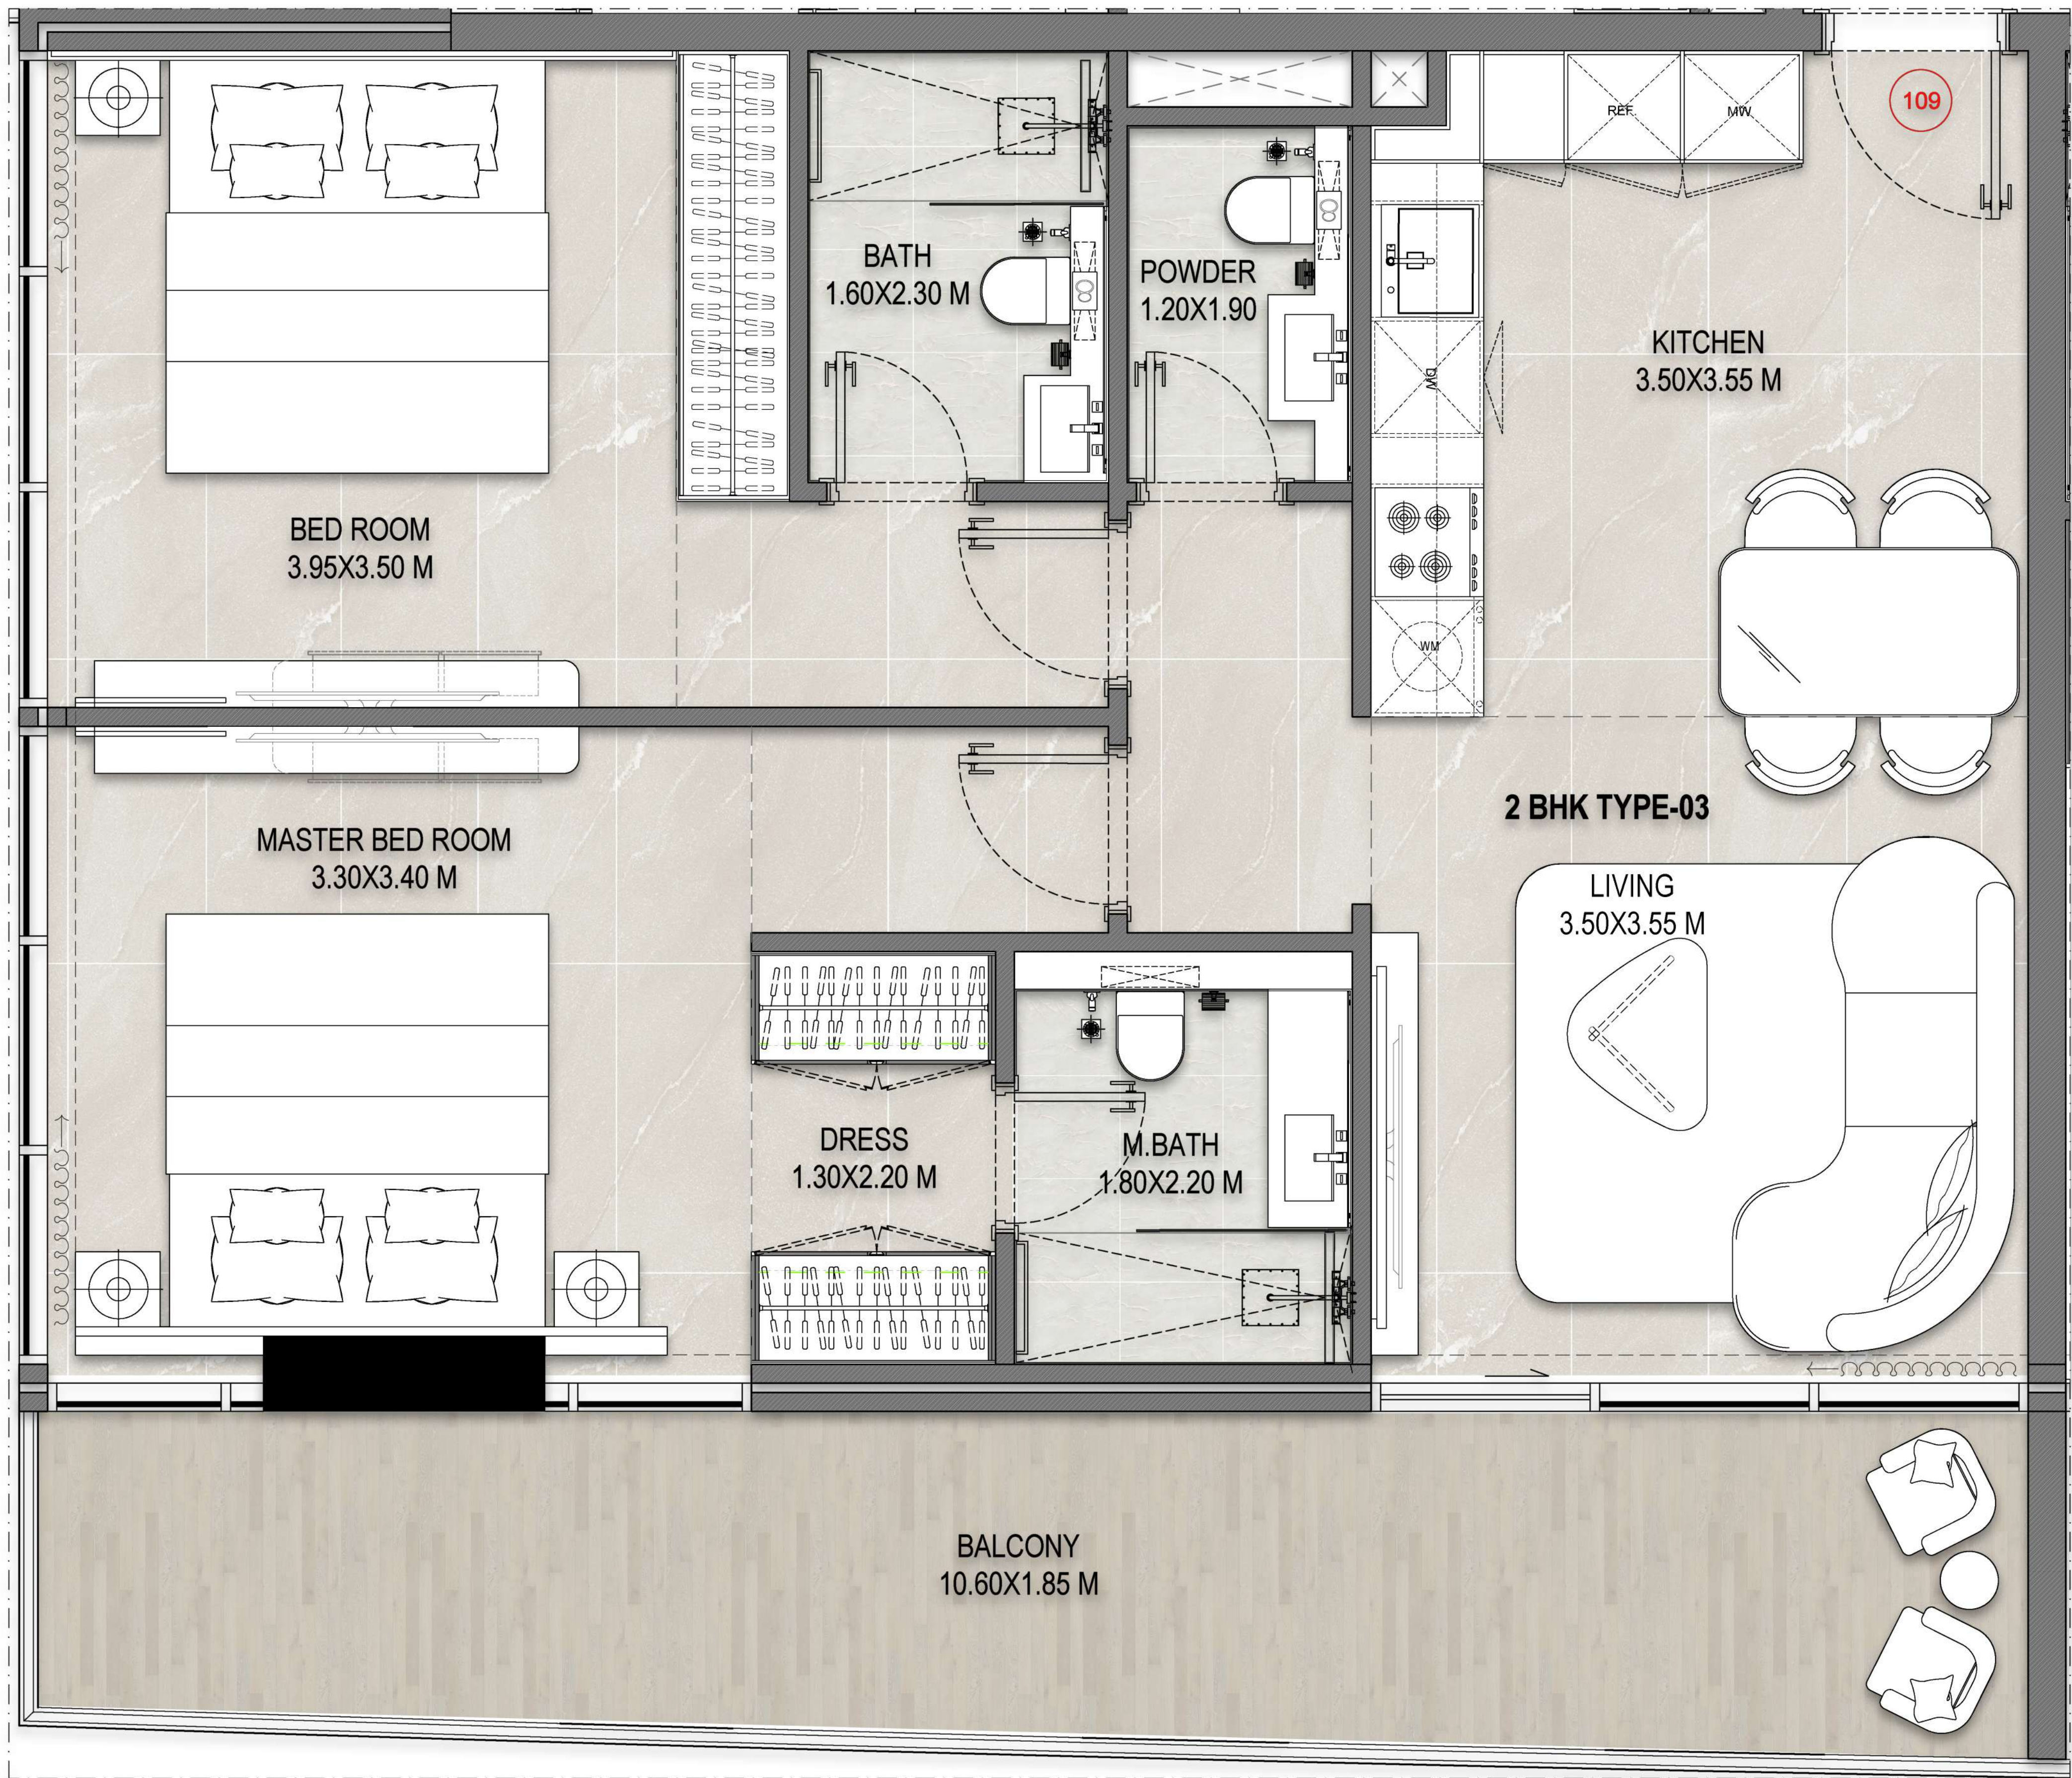

01 2BHK TYPE-03
SCALE 1:100@A1

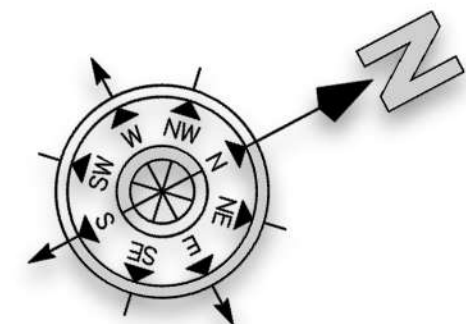

GENERAL NOTES :
DO NOT SCALE THIS DRAWING, ONLY STATED DIMENSIONS ARE TO BE CONSIDERED.
IT IS NOT ALLOWED TO COPY OR REPRODUCE IT'S CONTENTS IN ANY FORM EXCEPT FOR THE PURPOSE WHICH IT IS INTENDED WITHOUT THE ABOVE CONSULTANT'S AUTHORITY.
CONTRACTOR TO VERIFY THE DETAIL / INFORMATION GIVEN IN THIS DRAWING, ANY DISCREPANCIES SHALL BE BROUGHT TO ENGINEERS ATTENTION PRIOR TO COMMENCEMENT OF WORK, FAILURE TO COMPLY WITH THE ABOVE WILL BE CONTRACTORS LIABILITY.

CONSULTANT

INTERIOR DESIGNER



Rev.	Date	Description.	By
------	------	--------------	----

PURPOSE OF ISSUE
ISSUED FOR TENDER

PROJECT TITLE

G+04 RESIDENTIAL BUILDING

CLIENT

**ALASAD REAL ESTATE
DEVELOPMENT LLC**


PROJECT NO.
25-011 - Takmeel - Dubai South Building

DRAWING TITLE

2BHK TYPE-03

DATE	SHT. SIZE	SCALE	DRAWN	CHECKED	APPROVED
JUNE 2025	A1		CJA	YSR	YSR

PAGE NO	DRAWING ID	NORTH	REVISION
---------	------------	-------	----------

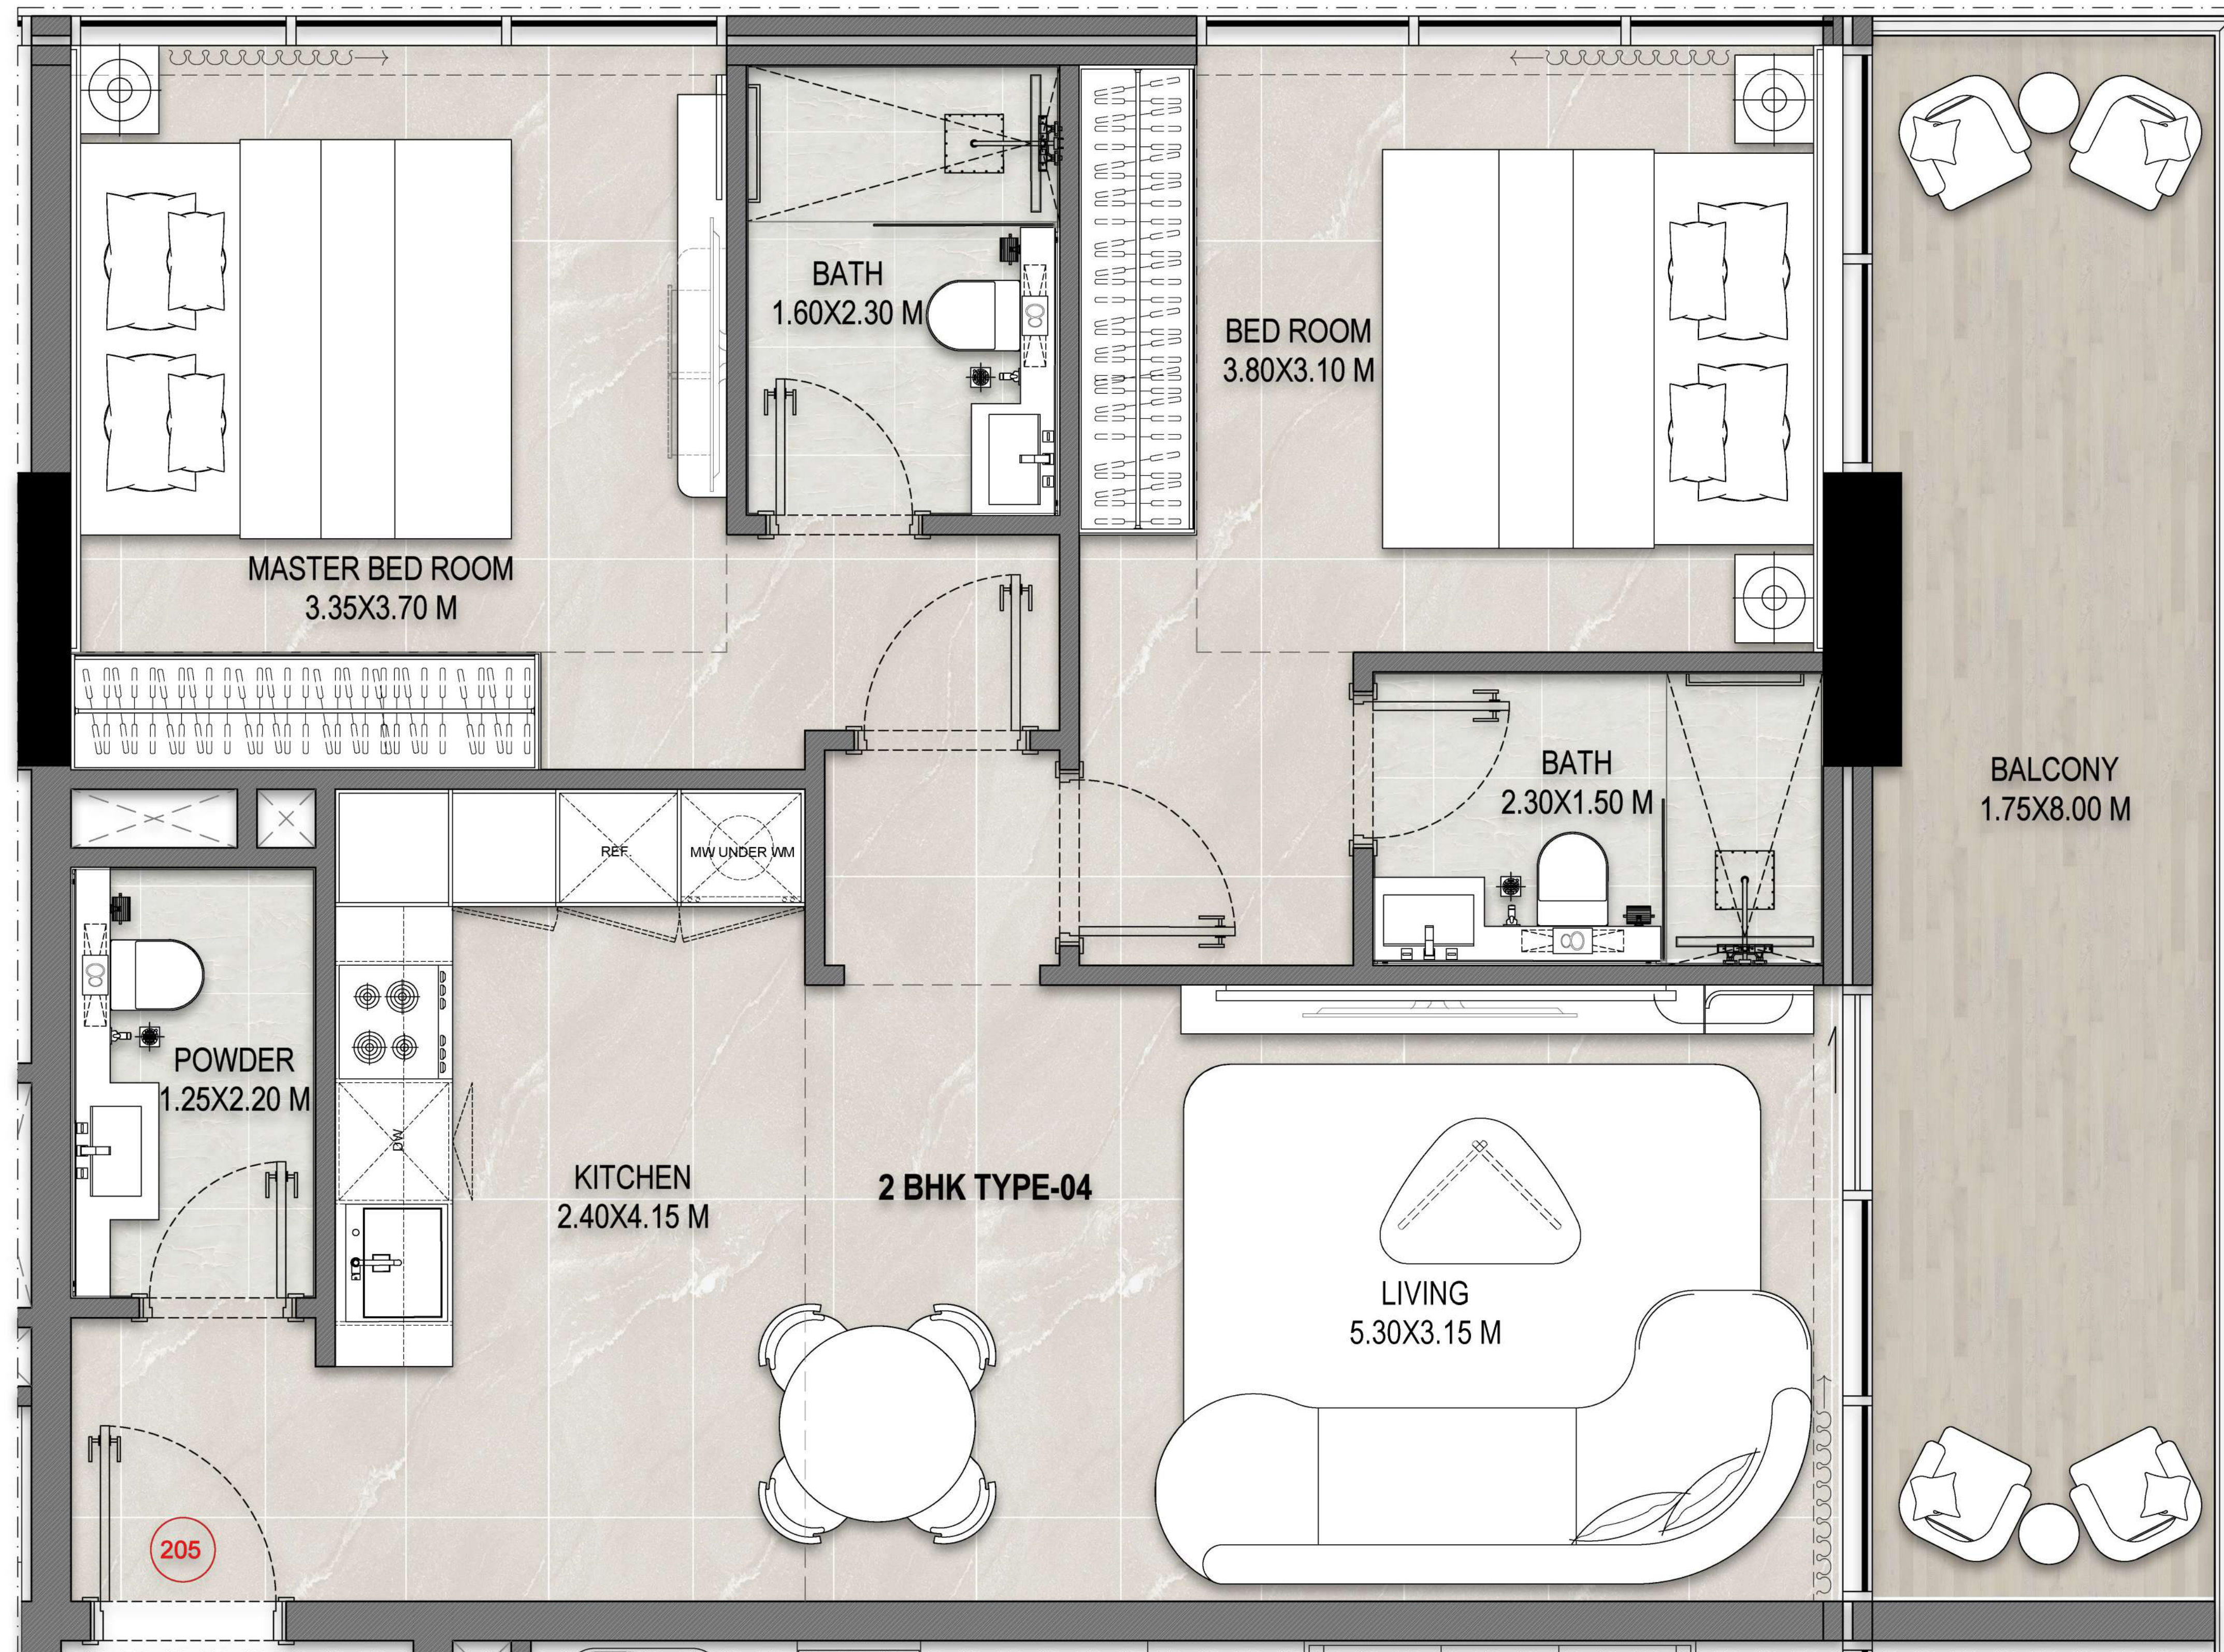

DATE	SHT. SIZE	SCALE	DRAWN	CHECKED	APPROVED
JUNE 2025	A1		CJA	YSR	YSR
PAGE NO	DRAWING ID			NORTH	REVISION